
SUPPLY SCOPE: the Nudura ICF formwork and accessories are our fixed price; every other package is the turnkey-kit BOQ, supplied in good faith from the model and to be checked by the relevant professional. Two storey: eaves 5,274, ridge 7,453 - householder planning permission.

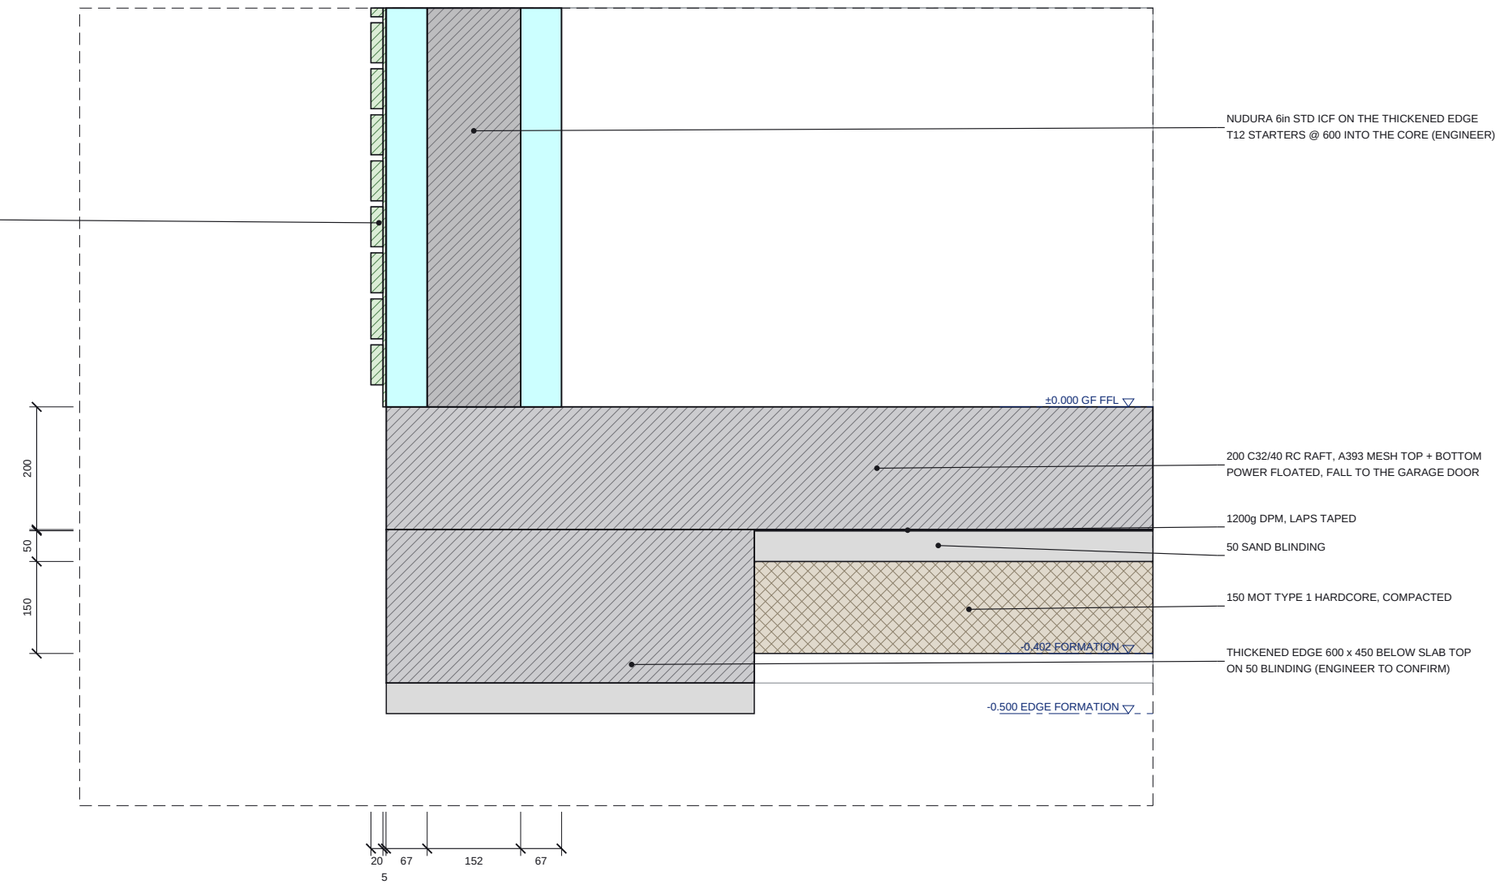

DETAIL 2: SLAB EDGE (WEST GABLE)

Scale 1:10 @ A3 | From Section B-B

NOTES

1. Blow-up of Section B-B at 1:10: the same model cut, cropped (dashed edge). Cut elements hatched / filled; the model beyond the cut in line work.
2. Levels above GF FFL.
3. Datum: 0 = raft slab top / garage floor. Client sheet size 6,500 x 7,500 -> Nudura Bond 6,483 x 7,499. Leeds / Yorkshire.

REVISIONS

REV	DATE	DESCRIPTION
Q01	28.10.26	First issue

Nudura™ BuildEase

CLIENT	PROJECT
Dortech Direct (James, MD) via Andy Claridge, Tremco CPG	Standard garage Type 04 - Brick two-storey double in Nudura ICF

DRAWING TITLE

SLAB EDGE DETAIL

Section B-B build-up detail

SCALE	SIZE	DATE
1:10	A3	28.10.26
DRAWN	CHECKED	APPROVED
TS		

STATUS	DRAWING No.	REV
QUOTATION	DG-T04-DT-02	Q01

Do not scale. All dimensions in millimetres; levels in metres from GF FFL. Check all dimensions on site.