
SUPPLY SCOPE: the Nudura ICF formwork and accessories are our fixed price; every other package is the turnkey-kit BOQ, supplied in good faith from the model and to be checked by the relevant professional. Single storey: eaves 2,496 < 2,500 and ridge 3,891 < 4,000 (Class E heights; check the 2 m boundary rule).

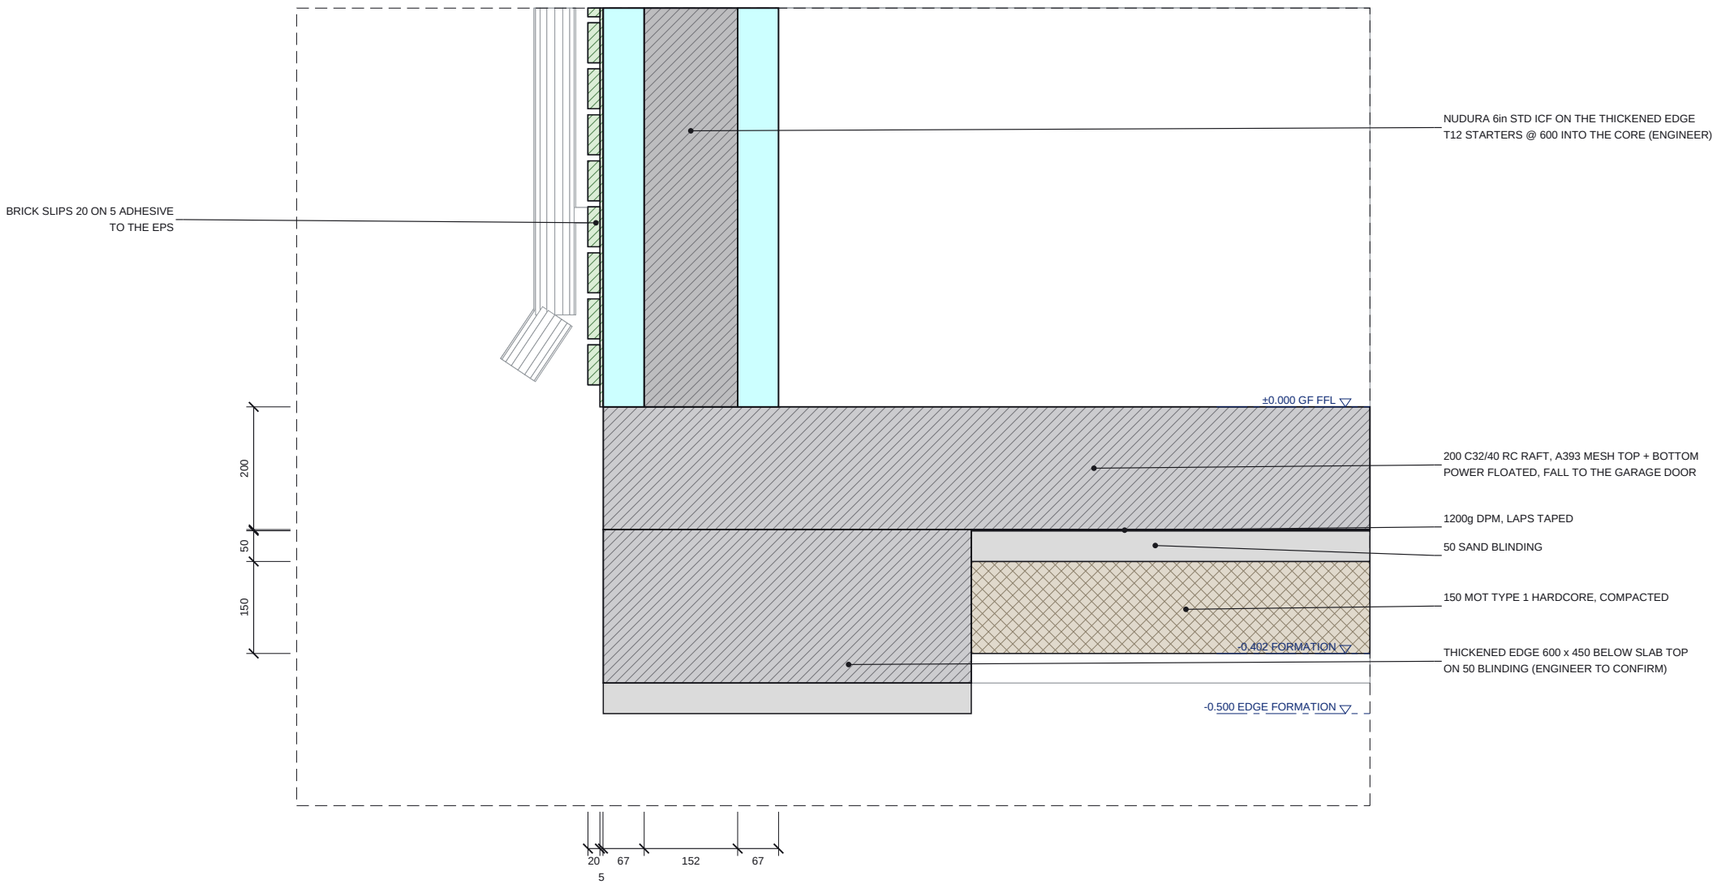

DETAIL 2: SLAB EDGE (LEFT WALL)

Scale 1:10 @ A3 | From Section A-A

Do not scale. All dimensions in millimetres, levels in metres from GF FFL. Check all dimensions on site.

NOTES

1. Blow-up of Section A-A at 1:10: the same model cut, cropped (dashed edge). Cut elements hatched / filled; the model beyond the cut in line work.
2. Levels above GF FFL.
3. Datum: 0 = raft slab top / garage floor. Client sheet size 6,500 x 6,000 -> Nudura Bond 6,483 x 6,077. Leeds / Yorkshire.

REVISIONS

REV	DATE	DESCRIPTION
Q01	28.10.26	First issue

Nudura™ BuildEase

CLIENT	PROJECT
Dortech Direct (James, MD) via Andy Claridge, Tremco CPG	Standard garage Type 02 - Brick double garage in Nudura ICF

DRAWING TITLE

SLAB EDGE DETAIL

Section A-A build-up detail

SCALE	SIZE	DATE
1:10	A3	28.10.26
DRAWN	CHECKED	APPROVED
TS		

STATUS	DRAWING No.	REV
QUOTATION	DG-T02-DT-02	Q01