

SUPPLY SCOPE: the Nudura ICF formwork and accessories are our fixed price; every other package is the turnkey-kit BOQ, supplied in good faith from the model and to be checked by the relevant professional. Single storey: eaves 2,488 < 2,500 and ridge 3,807 < 4,000 (Class E heights; check the 2 m boundary rule).

QUOTATION - NOT FOR CONSTRUCTION

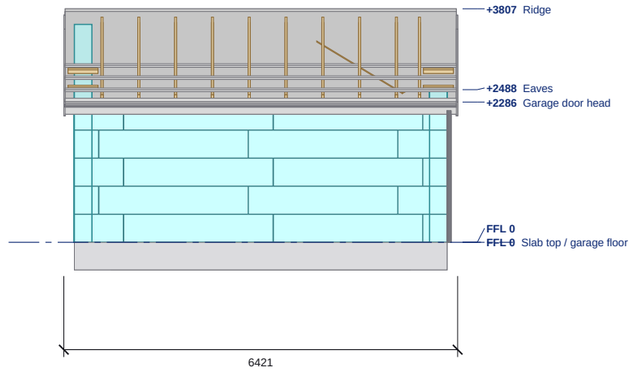

EAST SIDE ELEVATION

Scale 1:100 @ A3 | Levels above GF FFL; sills and heads in the schedule

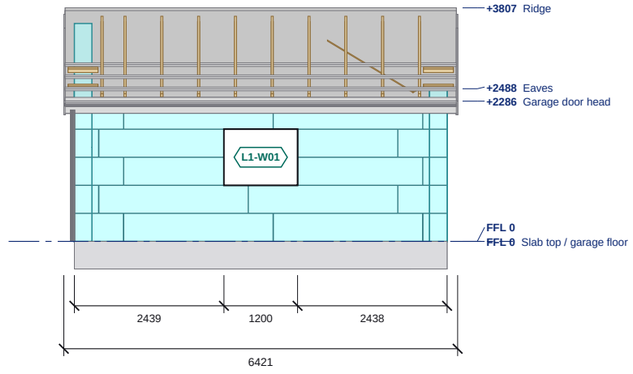

WEST SIDE ELEVATION

Scale 1:100 @ A3 | Levels above GF FFL; sills and heads in the schedule

0 1 2 3 4 5m

ICF external EPS face
Block course joint
Stack joint
Roof build-up (slab / earth / sedum)

Do not scale. All dimensions in millimetres, levels in metres from GF FFL. Check all dimensions on site.

ELEVATION SCHEDULES

EAST SIDE ELEVATION: OPENINGS

Ref	Width	Height	Sill	Head	Lintel
none					

Structural openings in the ICF; sill and head above GF FFL.

WEST SIDE ELEVATION: OPENINGS

Ref	Width	Height	Sill	Head	Lintel
L1-W01	1200	914	+914	+1829	-

Structural openings in the ICF; sill and head above GF FFL.

EAST SIDE ELEVATION: LEVELS

Level	FFL
Slab top / garage floor	0
underside of ICF	0
Garage door head	+2286
Eaves	+2488
Ridge	+3807

WEST SIDE ELEVATION: LEVELS

Level	FFL
Slab top / garage floor	0
underside of ICF	0
Garage door head	+2286
Eaves	+2488
Ridge	+3807

NOTES

1. ICF: Nudura 6" Std, 66.7 EPS + 152.4 core + 66.7 EPS = 285.8. External EPS face shown with the block course joints, vertical block joints and stack joints as populated.
2. Levels above GF FFL. Openings are structural openings in the ICF; glazing, doors, render and finishes by others, not shown.
3. Roof build-up shown as modelled.
4. See DG-T01-GA-01 for plan setting out, lintels and steel.
5. Datum: 0 = raft slab top / garage floor. Client sheet size 3,600 x 6,000 -> Nudura Bond 3,639 x 6,077. Leeds / Yorkshire.

REVISIONS

REV	DATE	DESCRIPTION
Q01	28.10.26	First issue

Nudura™ BuildEase

CLIENT	PROJECT
Dortech Direct (James, MD) via Andy Claridge, Tremco CPG	Standard garage Type 01 - Brick single garage in Nudura ICF

DRAWING TITLE

EAST AND WEST ELEVATIONS

ICF elevations with openings, levels and roof build-up

SCALE	SIZE	DATE
1:100	A3	28.10.26
DRAWN	**CHECKED**	**APPROVED**
TS		

STATUS	DRAWING No.	REV
QUOTATION	DG-T01-EL-02	Q01