
SUPPLY SCOPE: the Nudura ICF formwork and accessories are our fixed price; every other package is the turnkey-kit BOQ, supplied in good faith from the model and to be checked by the relevant professional. Single storey: eaves 2,488 < 2,500 and ridge 3,807 < 4,000 (Class E heights; check the 2 m boundary rule).

QUOTATION - NOT FOR CONSTRUCTION

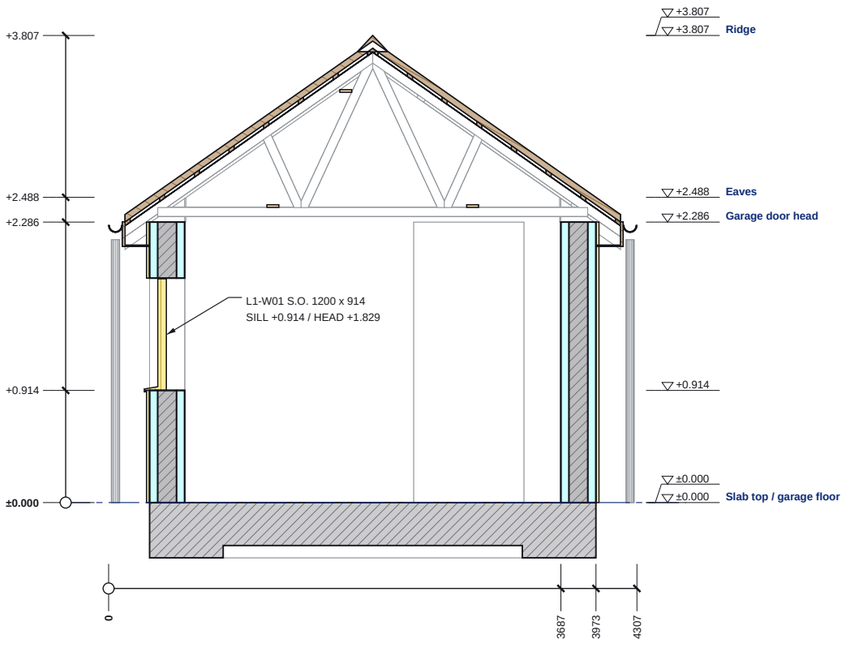

SECTION A-A

Scale 1:50 @ A3 | Looking north; levels above GF FFL

ICF EPS (cut)
ICF concrete core / RC (cut)
Steel (cut)
Beyond the cut (line work)


0 1 2m

SECTION A-A SCHEDULES

LEVELS ON THIS SECTION

Level	FFL
Slab top / garage floor	±0.000
top of ICF W01	+0.914
Garage door head	+2.286
Eaves	+2.488
Ridge	+3.807

SECTION KEY

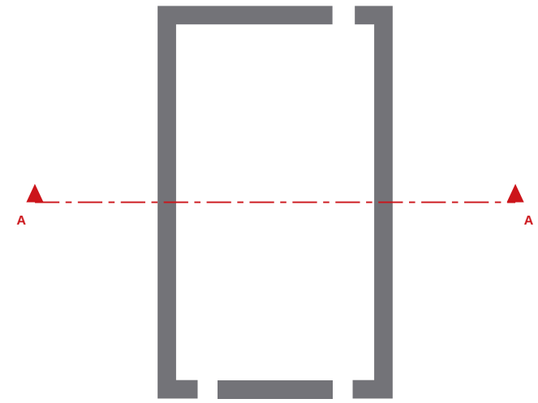

NOTES

1. Section A-A is a BuildEase ICF section (not an architect's section line). Cut elements hatched / filled; the model beyond the cut in line work.
2. Levels above GF FFL.
3. ICF: Nudura 6" Std, 66.7 EPS + 152.4 core + 66.7 EPS = 285.8, 152.4 core + 66.7 EPS = 285.8. No structural design yet: raft slab, garage door lintel (one full course), roof and floor - engineer to confirm.
4. Steel marks, BOS / TOS: rev -. See DG-T01-GA-01 / EL-01 / EL-02 in the approval drawings pack.
5. Datum: 0 = raft slab top / garage floor. Client sheet size 3,600 x 6,000 -> Nudura Bond 3,639 x 6,077. Leeds / Yorkshire.

REVISIONS

REV	DATE	DESCRIPTION
Q01	28.10.26	First issue

Nudura™ BuildEase

CLIENT	PROJECT
Dortech Direct (James, MD) via Andy Claridge, Tremco CPG	Standard garage Type 01 - Brick single garage in Nudura ICF

DRAWING TITLE

SECTION A-A

ICF section with levels and build-ups

SCALE	SIZE	DATE
1:50	A3	28.10.26
DRAWN	CHECKED	APPROVED
TS		

STATUS	DRAWING No.	REV
QUOTATION	DG-T01-SE-01	Q01

Do not scale. All dimensions in millimetres, levels in metres from GF FFL. Check all dimensions on site.