SUPPLY SCOPE: the Nudura ICF formwork and accessories are our fixed price; every other package is the turnkey-kit BOQ, supplied in good faith from the model and to be checked by the relevant professional. Single storey: eaves 2,496 < 2,500 and ridge 3,891 < 4,000 (Class E heights; check the 2 m boundary rule).

QUOTATION - NOT FOR CONSTRUCTION

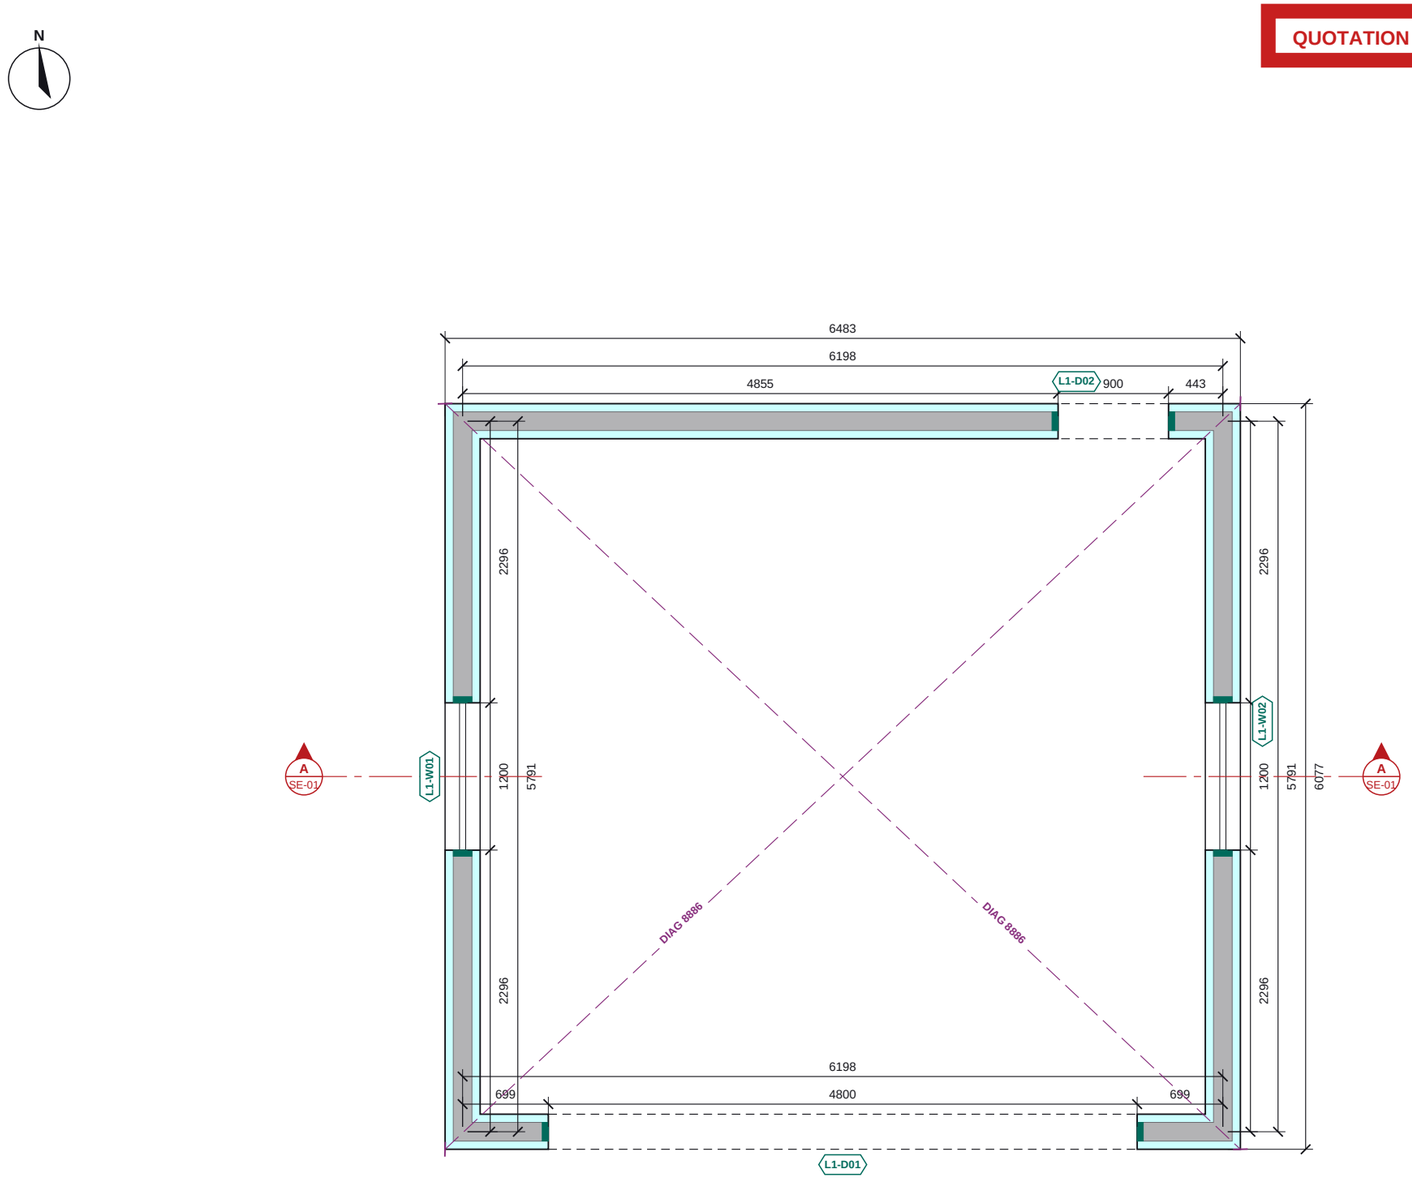

GROUND FLOOR ICF PLAN

Scale 1:50 @ A3 | Plan cut at 1200 above GF FFL

0 1 2 3m

EPS insulation (Nudura form)
Concrete core
End cap at opening
Engineer's pier bars (n-H12 vertical bars in ICF pier) / WS wall starters
Setting-out check diagonal (external ICF corners)
Section line (see SE sheet)

GROUND FLOOR ICF SCHEDULES

OPENING SCHEDULE

Ref	Width	Height	Sill	Head	Lintel
L1-D01	4800	2286	0	+2286	-
L1-D02	900	2286	0	+2286	-
L1-W01	1200	914	+914	+1829	-
L1-W02	1200	914	+914	+1829	-

Structural openings in the ICF; sill and head above GF FFL.

NOTES

1. ICF: Nudura 6" Std, 66.7 EPS + 152.4 core + 66.7 EPS = 285.8. Dimensions to the ICF faces.
2. Levels above GF FFL. Sill / head = structural opening in the ICF.
3. No structural design yet: raft slab, garage door lintel (one full course), roof and floor - engineer to confirm.
4. Lintel (L-n) and steel (B-n, C-1) marks from rev -, which takes precedence.
5. Masonry walls shown for context.
6. Datum: 0 = raft slab top / garage floor. Client sheet size 6,500 x 6,000 -> Nudura Bond 6,483 x 6,077. Leeds / Yorkshire.

REVISIONS

REV	DATE	DESCRIPTION
Q01	28.10.26	First issue

Nudura™ BuildEase

CLIENT	PROJECT
Dortech Direct (James, MD) via Andy Claridge, Tremco CPG	Standard garage Type 06 - Rendered double garage in Nudura ICF

DRAWING TITLE

GARAGE ICF GENERAL ARRANGEMENT

ICF walls, openings, lintels, steel over and engineer's notes

SCALE	SIZE	DATE
1:50	A3	28.10.26
DRAWN	CHECKED	APPROVED
TS		

STATUS	DRAWING No.	REV
QUOTATION	DG-T06-GA-01	Q01

Do not scale. All dimensions in millimetres; levels in metres from GF FFL. Check all dimensions on site.